




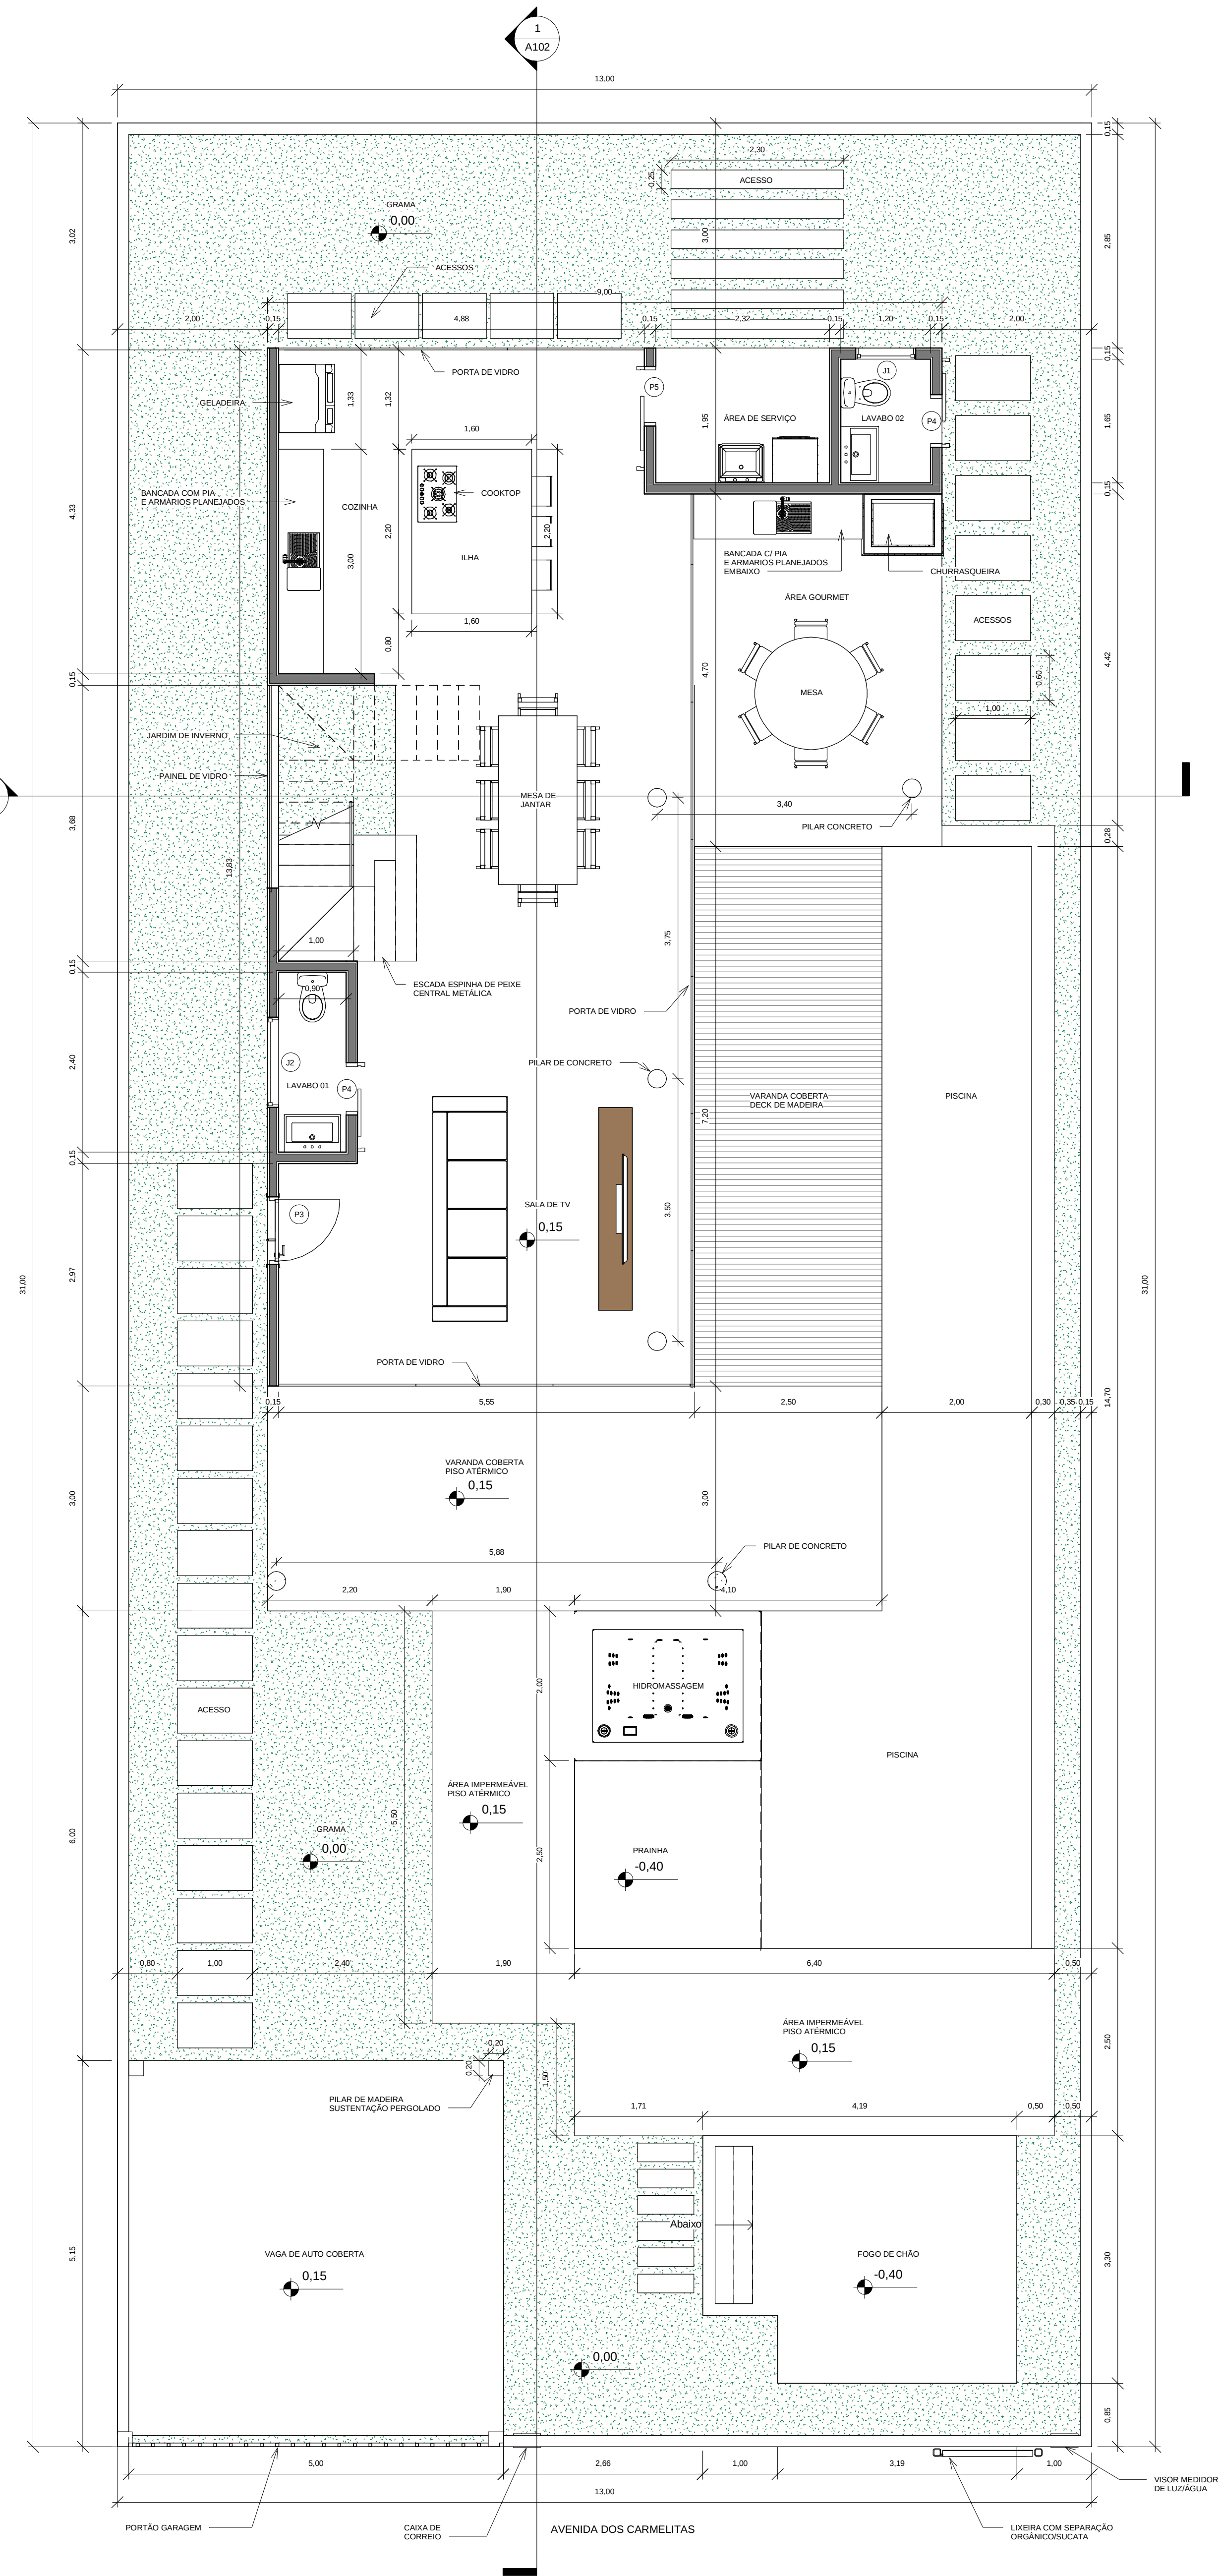

1 IMPLANTAÇÃO E PÁV.01
1 : 50

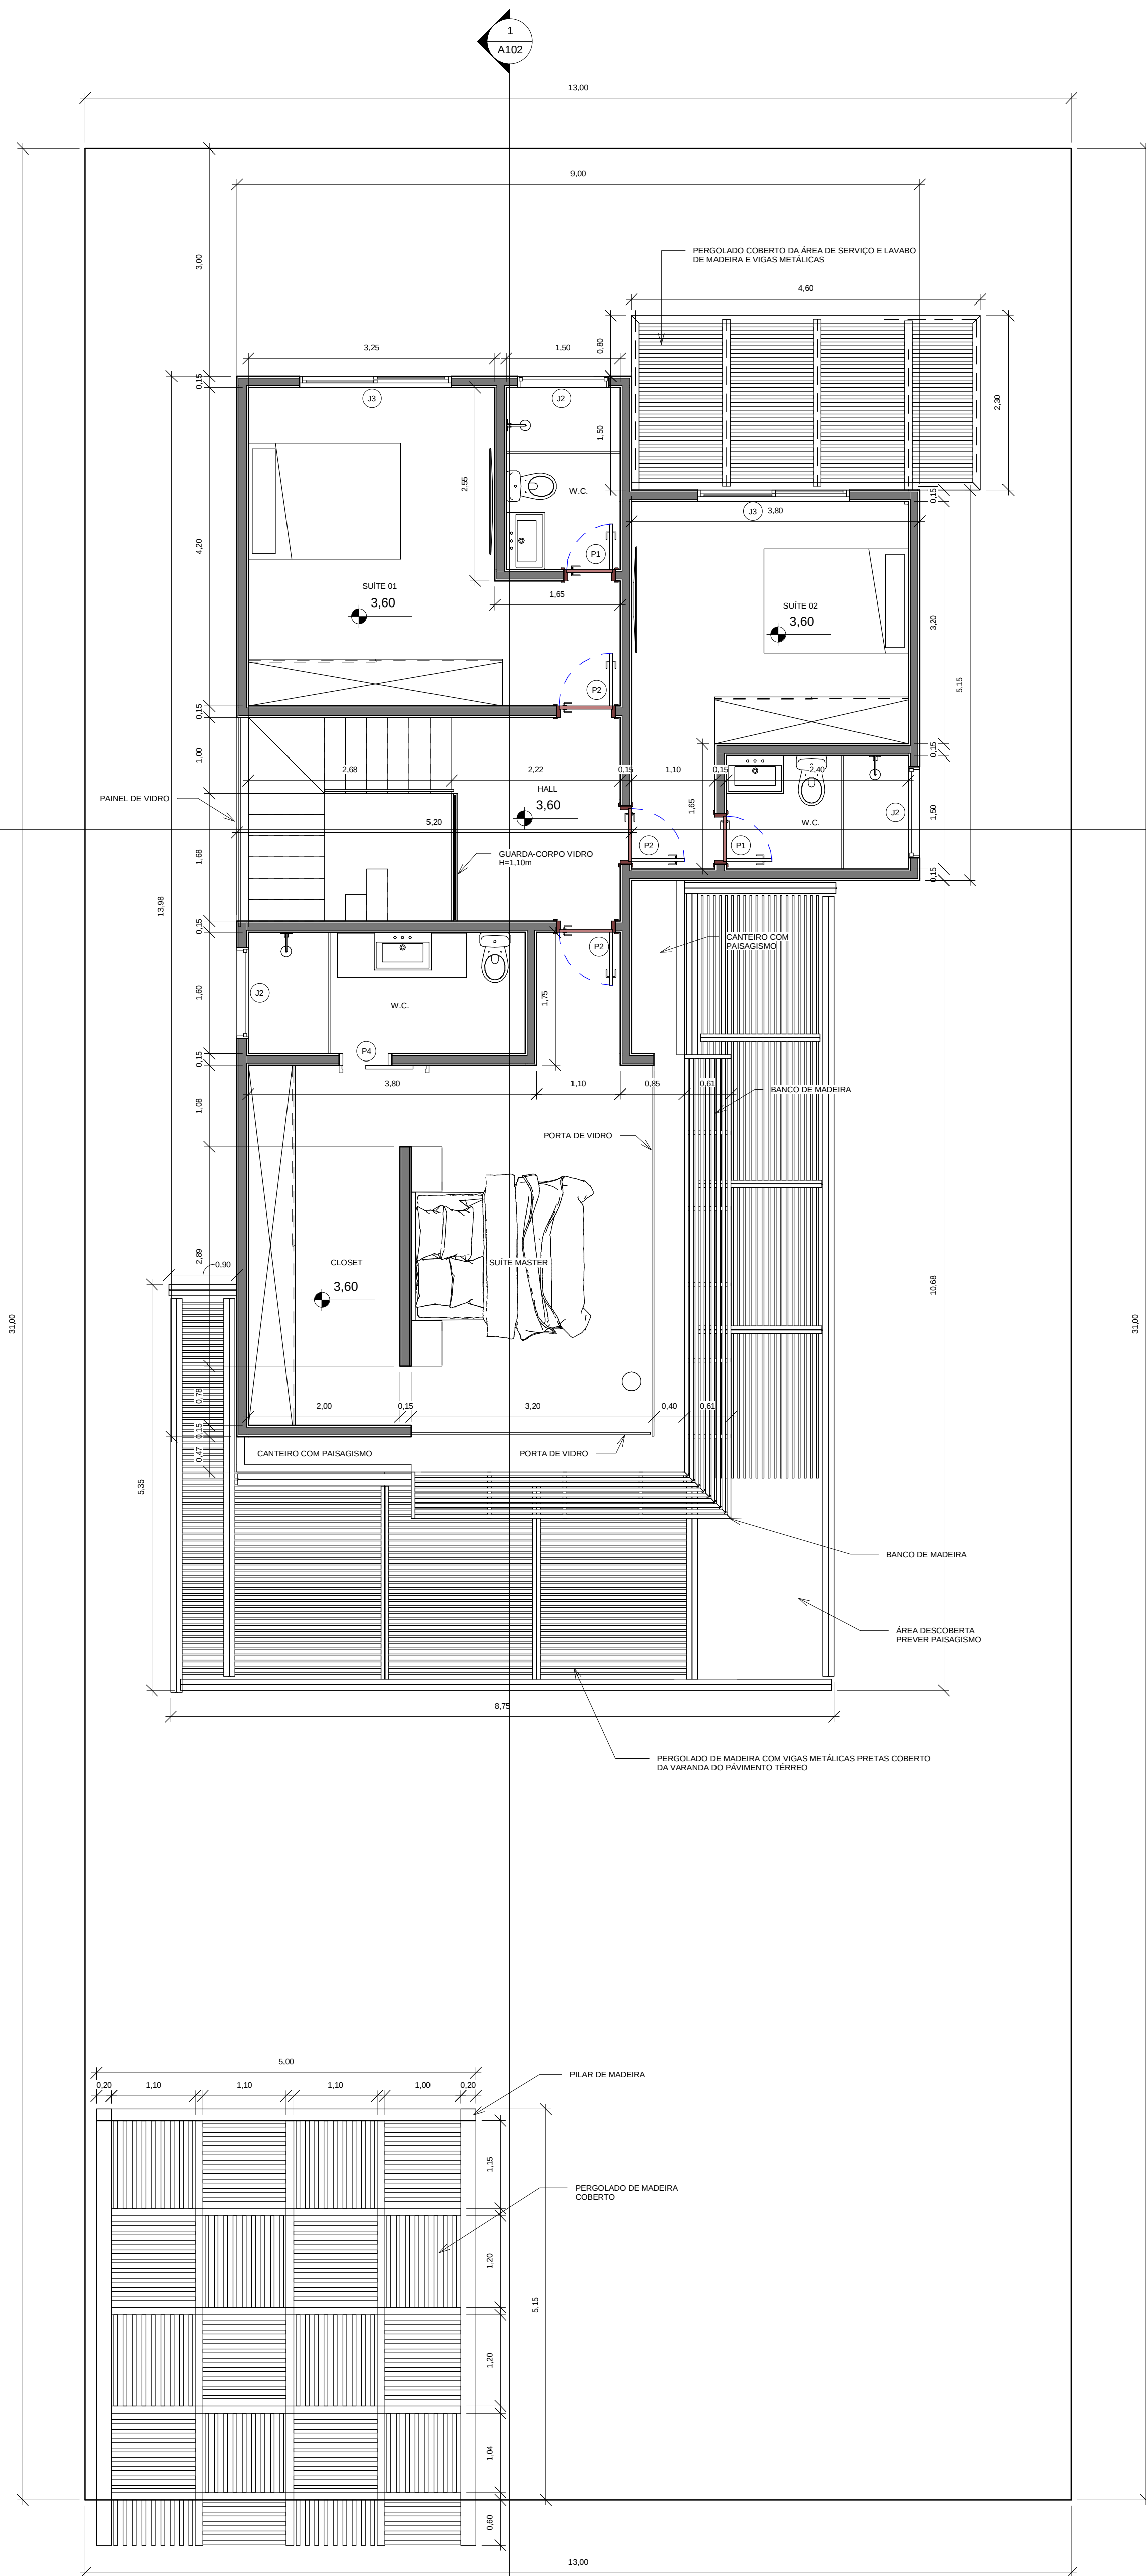

2 IMPLANTAÇÃO E PÁV.02
1 : 50

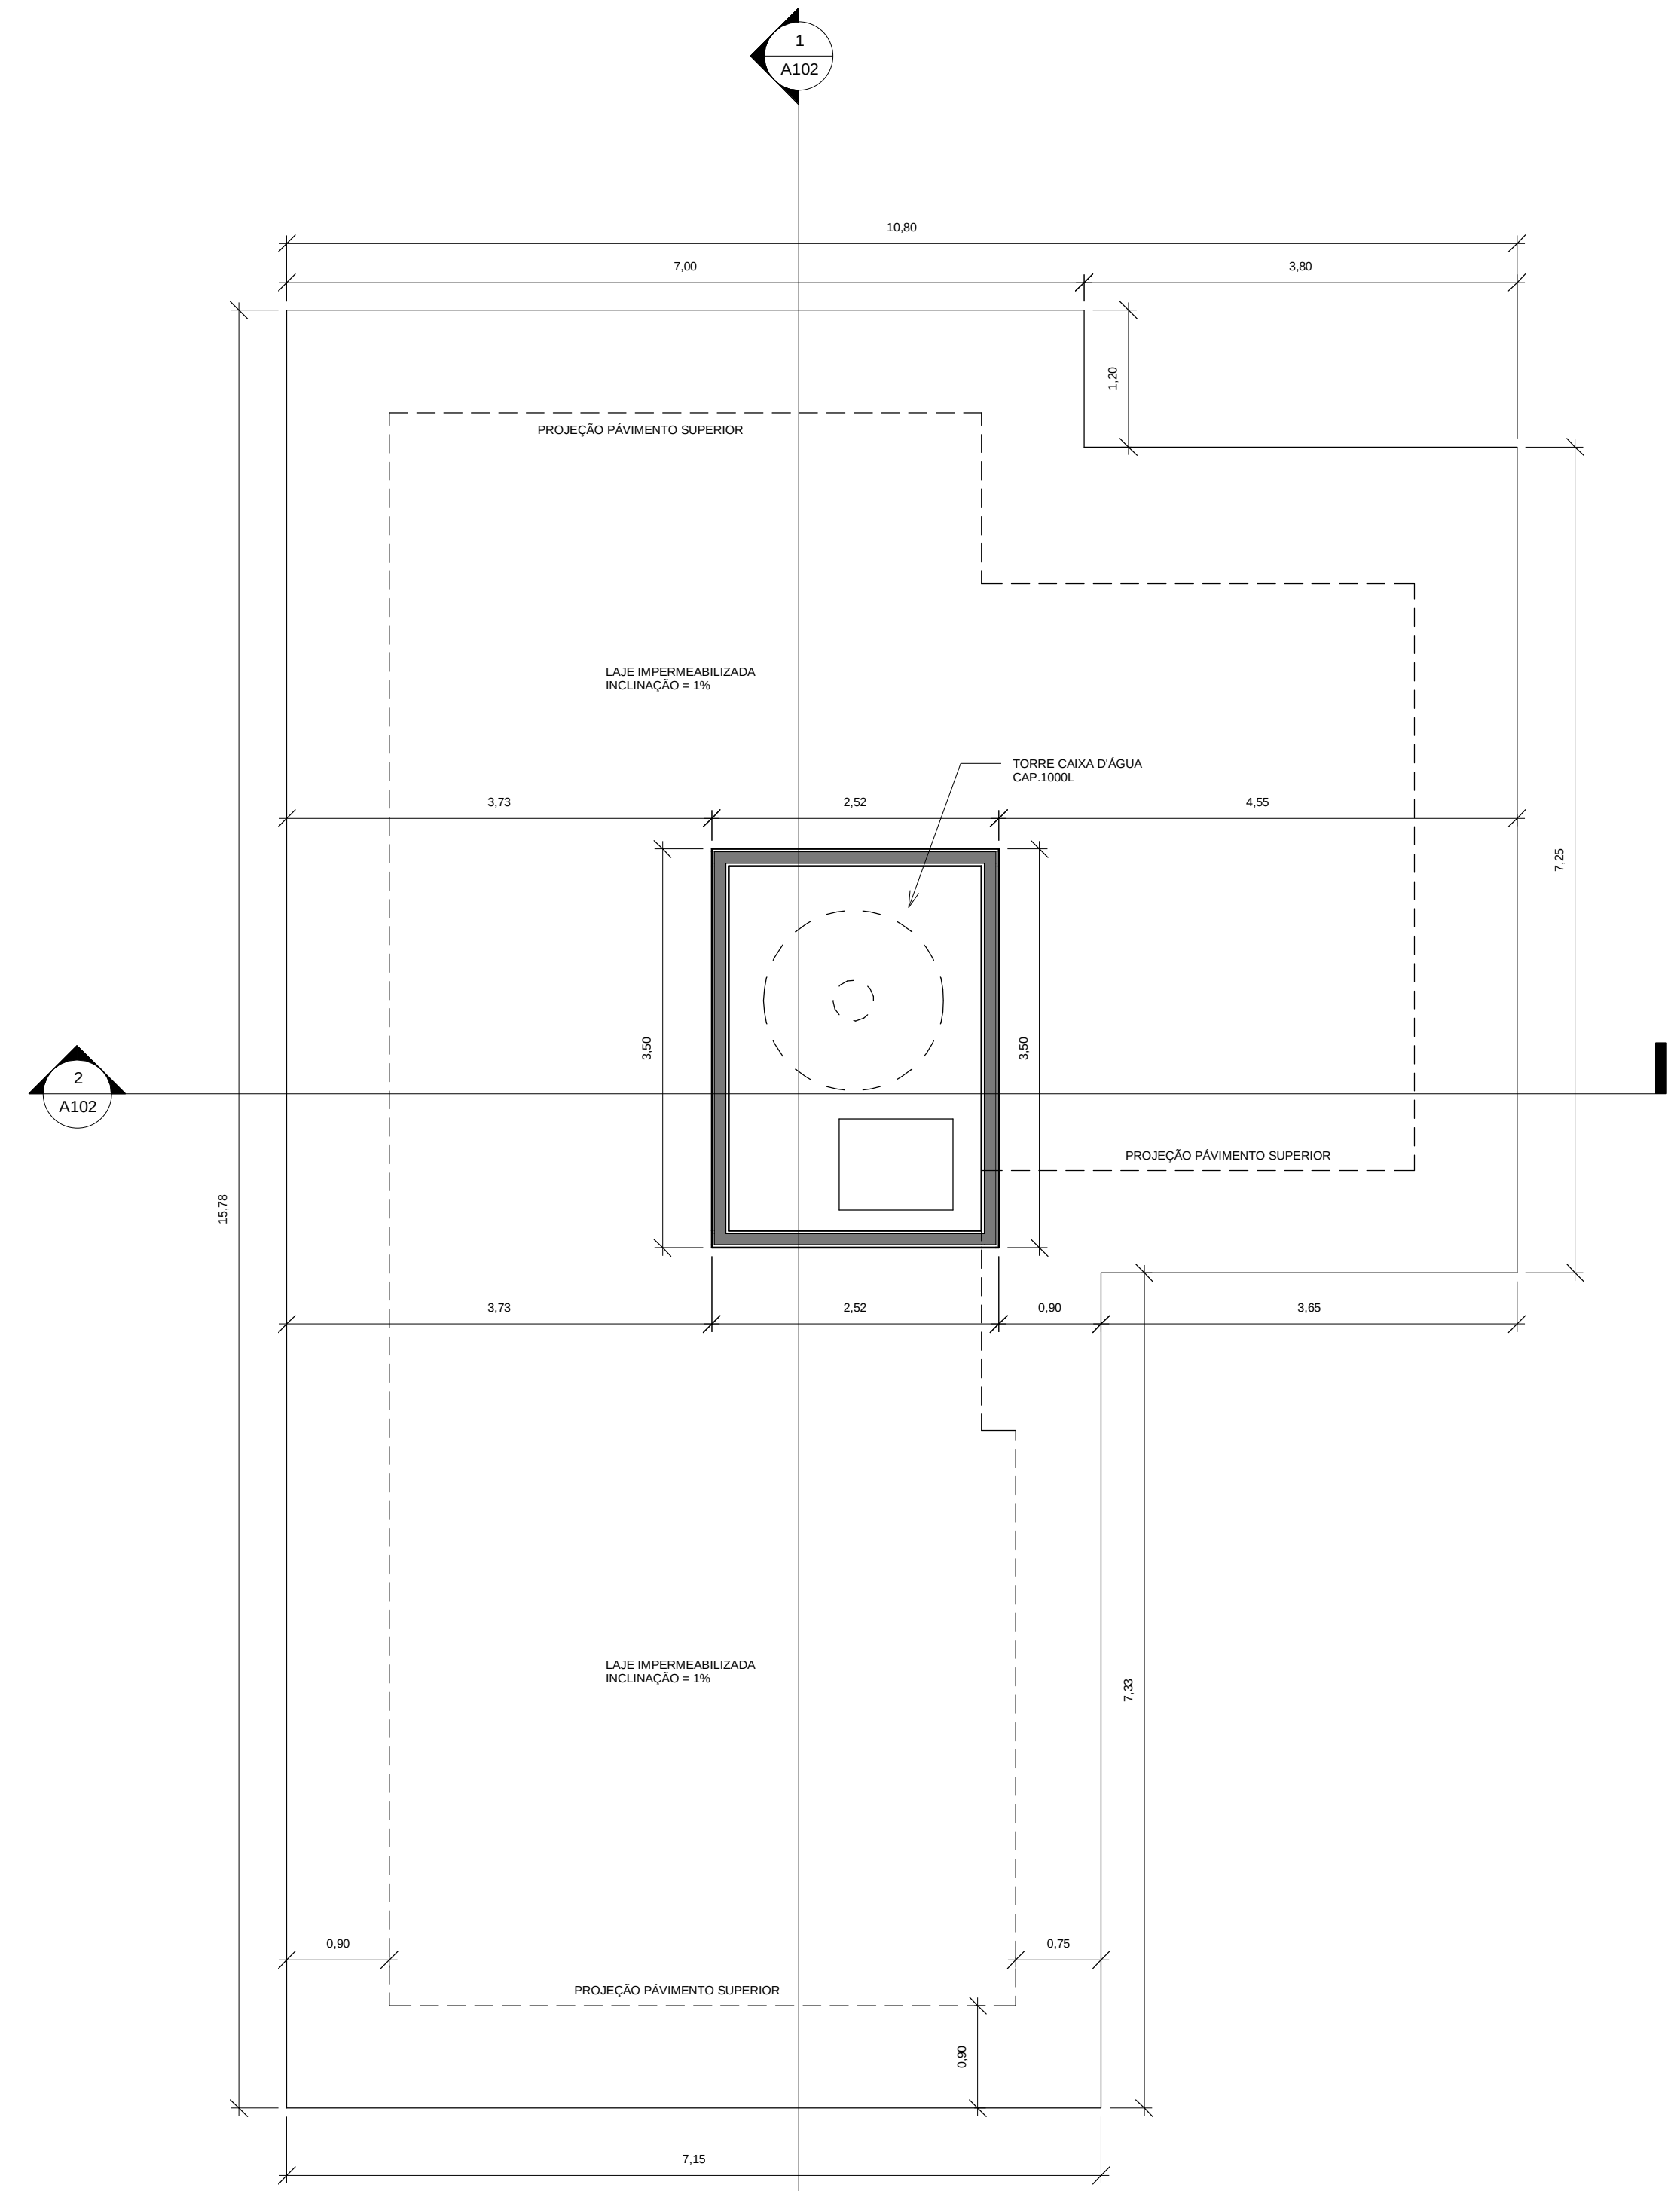


3 COBERTURA
1 : 50

TABELA DE AMBIENTES		
AMBIENTE	ÁREA	NÍVEL
GARAGEM	25,64 m²	IMPLANTAÇÃO E PÁV.01
FOGO DE CHÃO	12,95 m²	IMPLANTAÇÃO E PÁV.01
VARANDA COBERTA	24,37 m²	IMPLANTAÇÃO E PÁV.01
LAVABO 01	2,15 m²	IMPLANTAÇÃO E PÁV.01
SALA DE TV	28,54 m²	IMPLANTAÇÃO E PÁV.01
SALA DE JANTAR	29,37 m²	IMPLANTAÇÃO E PÁV.01
COZINHA	23,60 m²	IMPLANTAÇÃO E PÁV.01
ÁREA DE SERVIÇO	4,18 m²	IMPLANTAÇÃO E PÁV.01
LAVABO 02	1,98 m²	IMPLANTAÇÃO E PÁV.01
ÁREA GOURMET	15,46 m²	IMPLANTAÇÃO E PÁV.01
DECK DE MADEIRA	18,00 m²	IMPLANTAÇÃO E PÁV.01
PISCINA	47,86 m²	IMPLANTAÇÃO E PÁV.01
SUITE MASTER	27,06 m²	IMPLANTAÇÃO E PÁV.02
W.C. SUITE MASTER	5,85 m²	IMPLANTAÇÃO E PÁV.02
HALL	5,95 m²	IMPLANTAÇÃO E PÁV.02
SUITE 02	13,50 m²	IMPLANTAÇÃO E PÁV.02
W.C. SUITE 02	3,60 m²	IMPLANTAÇÃO E PÁV.02
SUITE 01	16,37 m²	IMPLANTAÇÃO E PÁV.02
W.C. SUITE 01	3,60 m²	IMPLANTAÇÃO E PÁV.02
Grand total: 19		30,02 m²


QUADRO DE ESQUADRIAS - PORTAS				
TIPO	QUANTIDADE	LARGURA	ALTURA	DESCRIÇÃO
P1	2	0,60	2,10	ABRIR / 01 FOLHA
P2	3	0,70	2,10	ABRIR / 01 FOLHA
P3	1	0,90	2,10	ABRIR / 01 FOLHA
P4	3	0,70	2,10	DE CORRER - 01 FOLHA
P5	1	0,80	2,10	DE CORRER - 02 FOLHAS
P6	1	1,20	1,20	LUXEIRA
Grand total: 11				

QUADRO DE ESQUADRIAS - JANELAS				
TIPO	QUANTIDADE	LARGURA	ALTURA	DESCRIÇÃO
J1	1	0,90	0,90	MAXIMAR
J2	4	1,20	0,90	MAXIMAR
J3	2	2,00	1,00	DE CORRER - 02 FOLHAS
Grand total: 7				


PROJETO:	TÉCNICO
PROPRIETÁRIO:	DOUGLAS ALBERTO BRAGA
LOCAL:	GUACECÁ - SP
ASSUNTO:	PLANTAS TÉCNICAS
Arquiteto:	PAULO GVOZDEN
CONTATO:	12- 99192 3445
ESCALA	1 : 50 DATA 2022 FOLHA A0

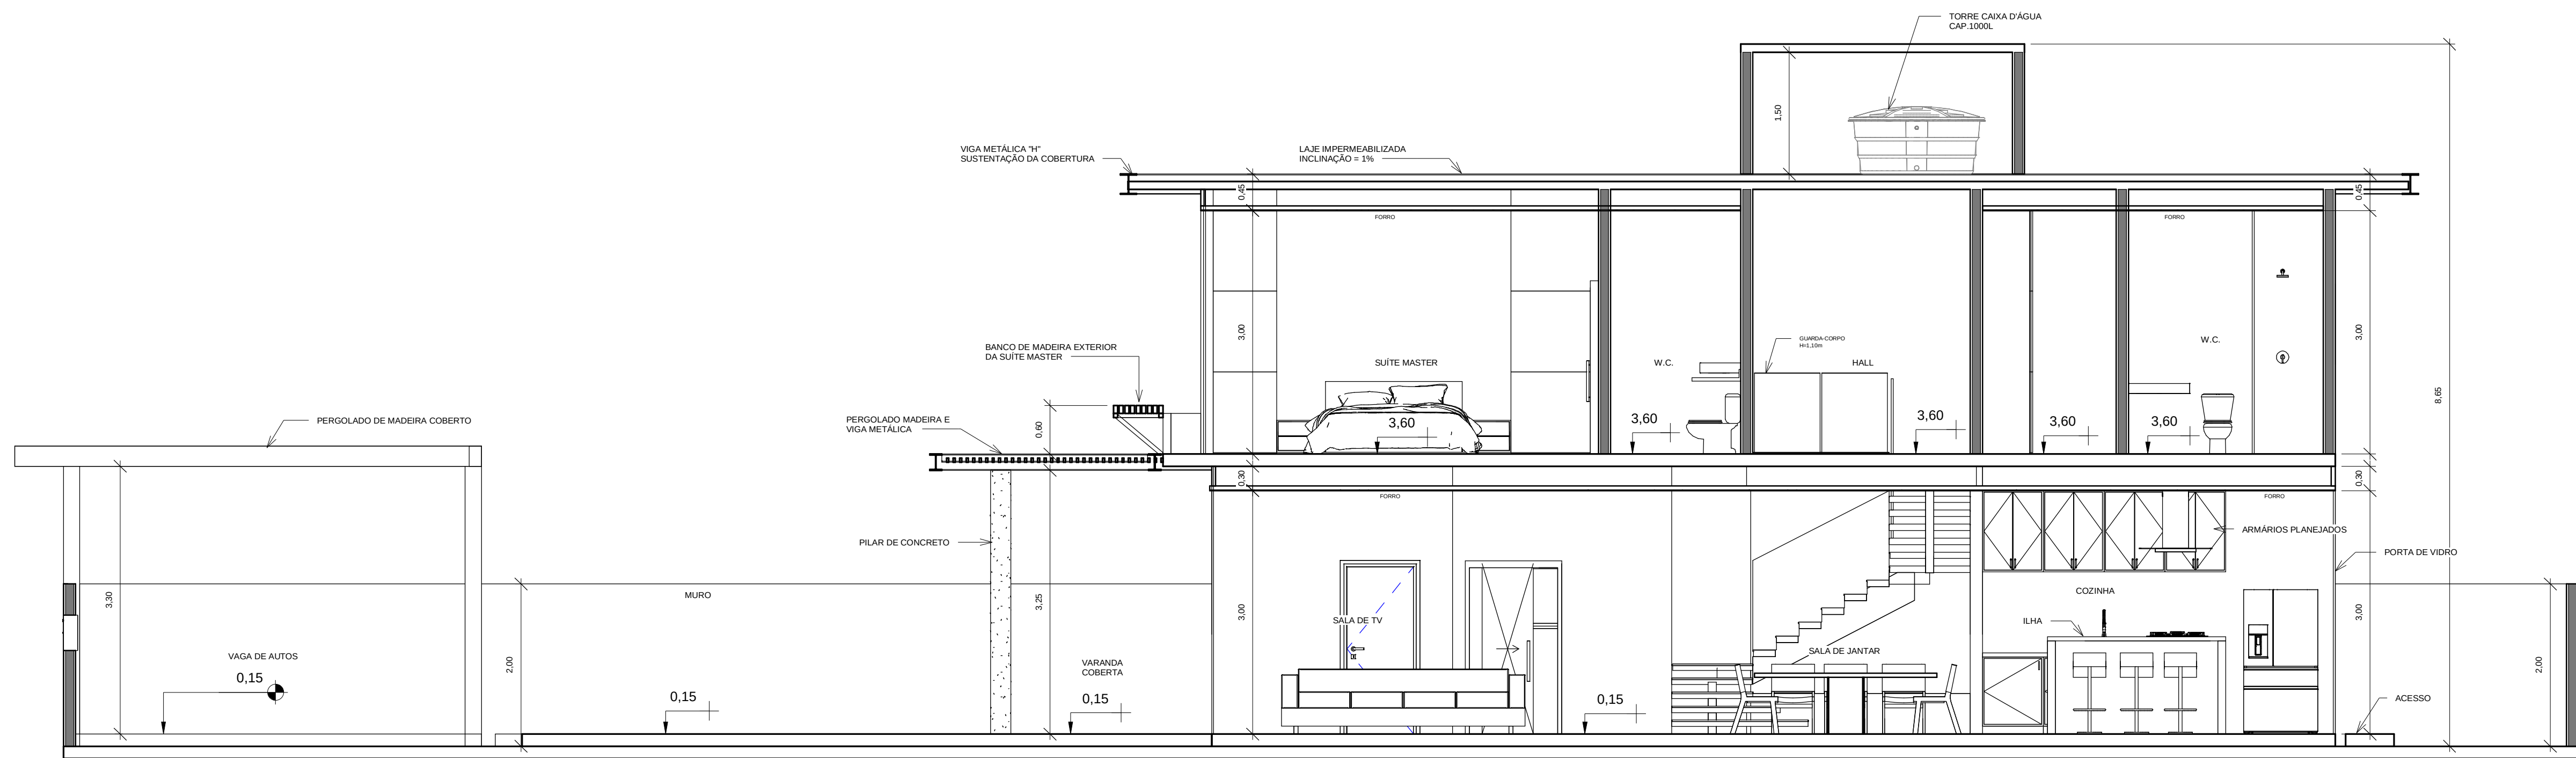


1 CORTE AA
1 : 50

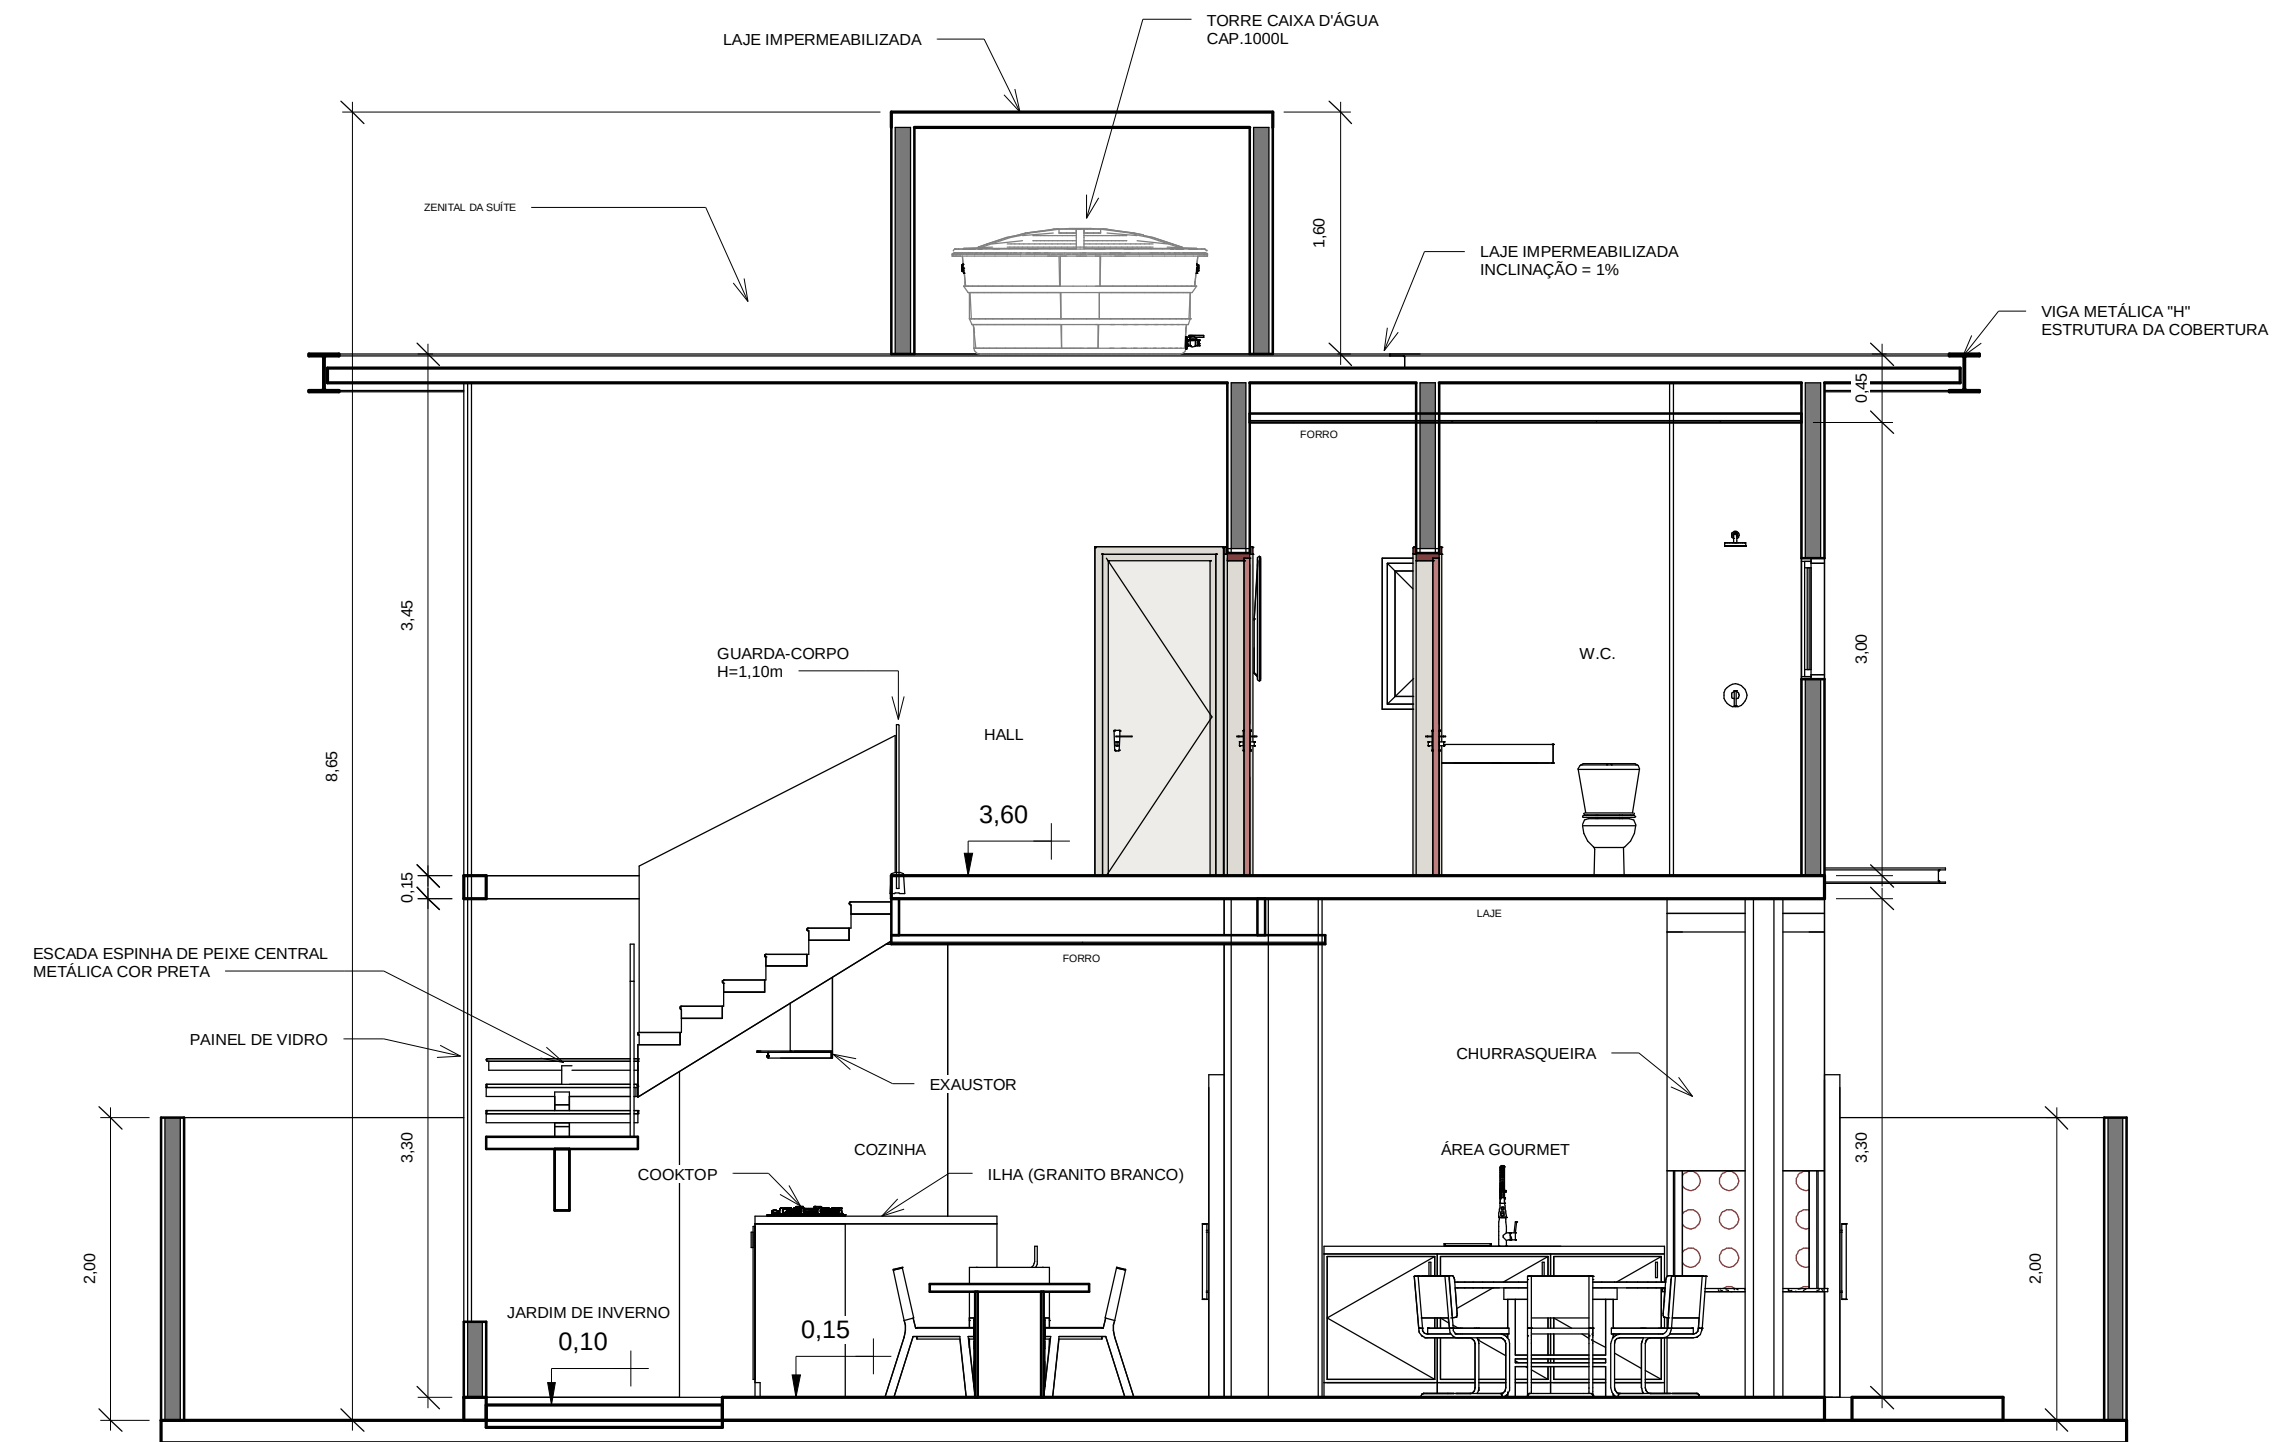

2 CORTE BB
1 : 50

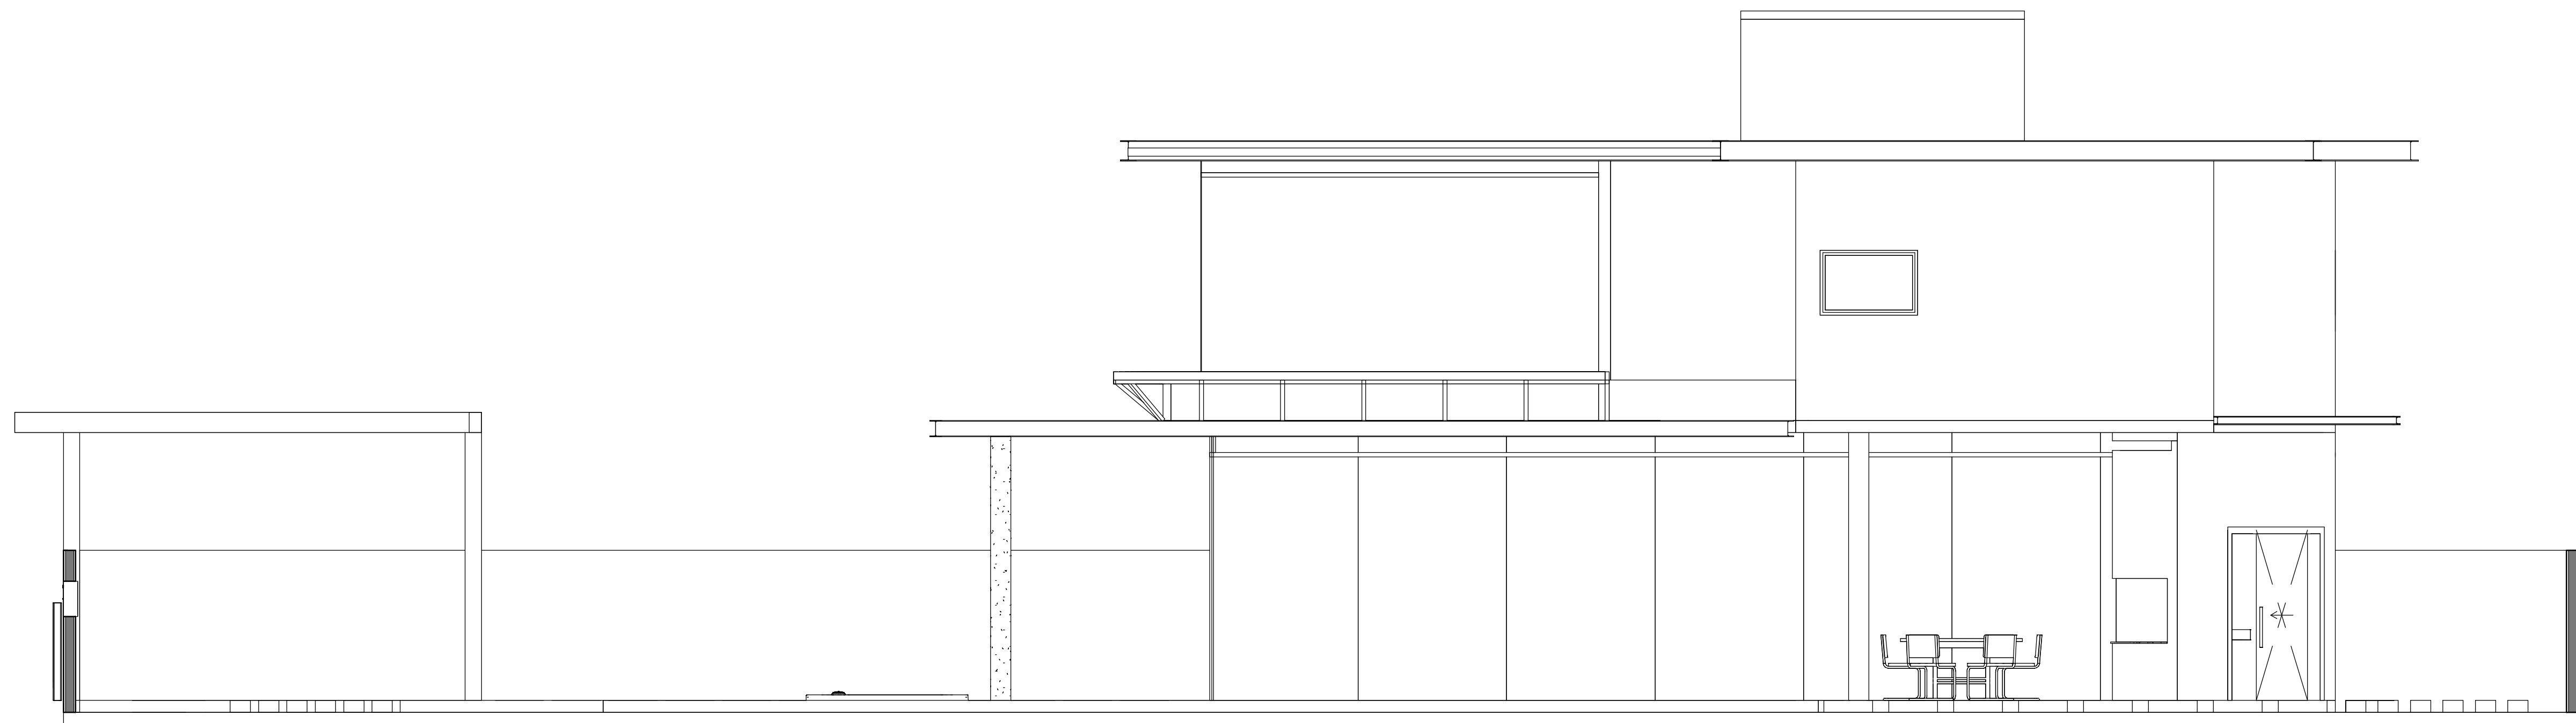

4 FACHADA LATERAL
1 : 50

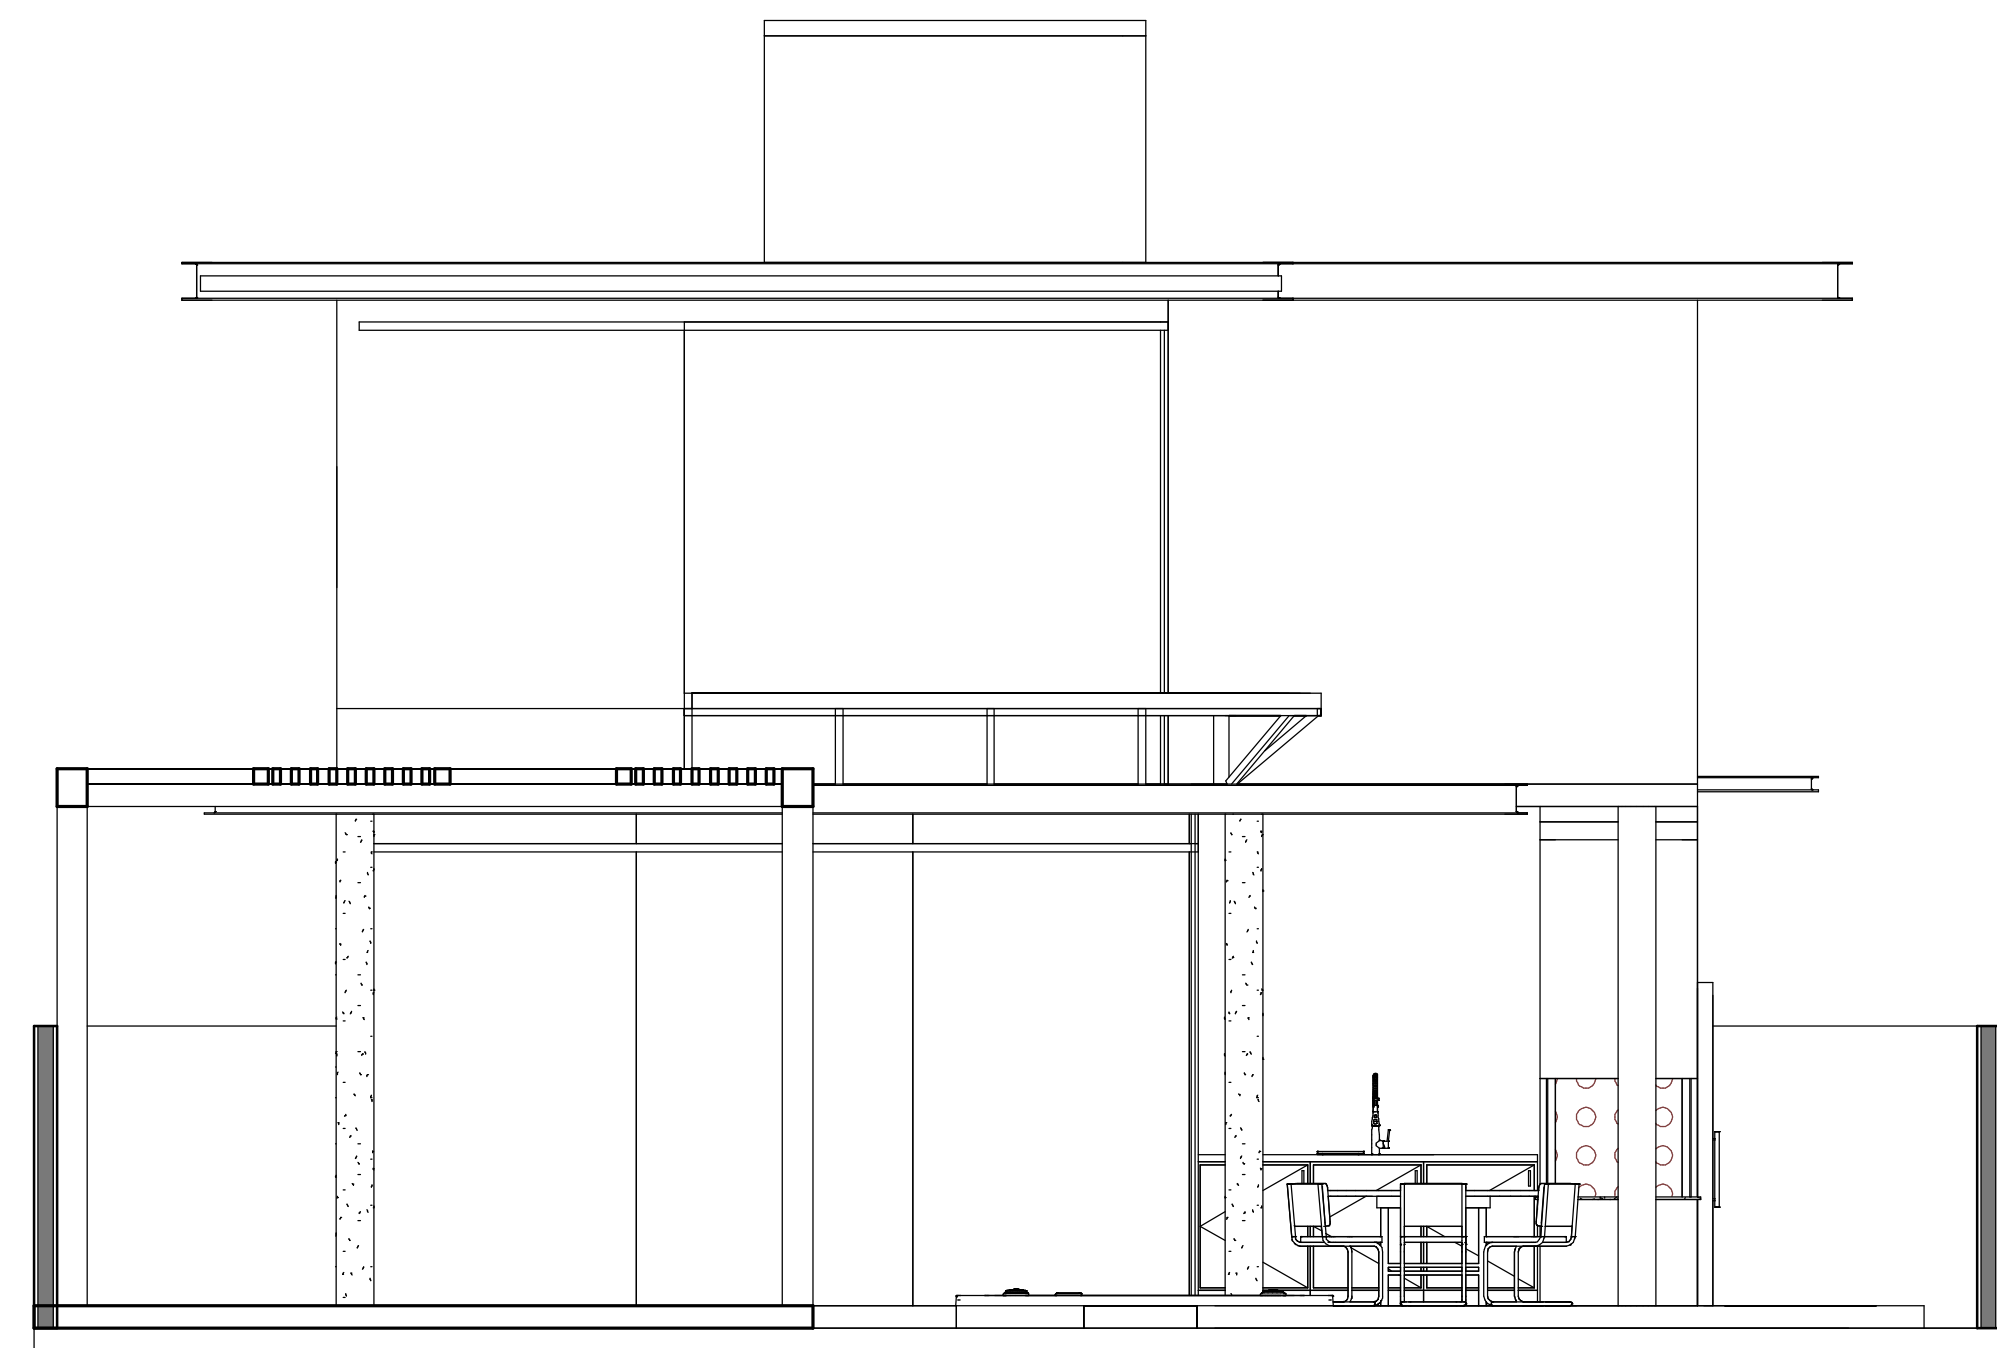


3 FACHADA FRONTAL
1 : 50



5 PERSPECTIVA 01



6 PERSPECTIVA 02

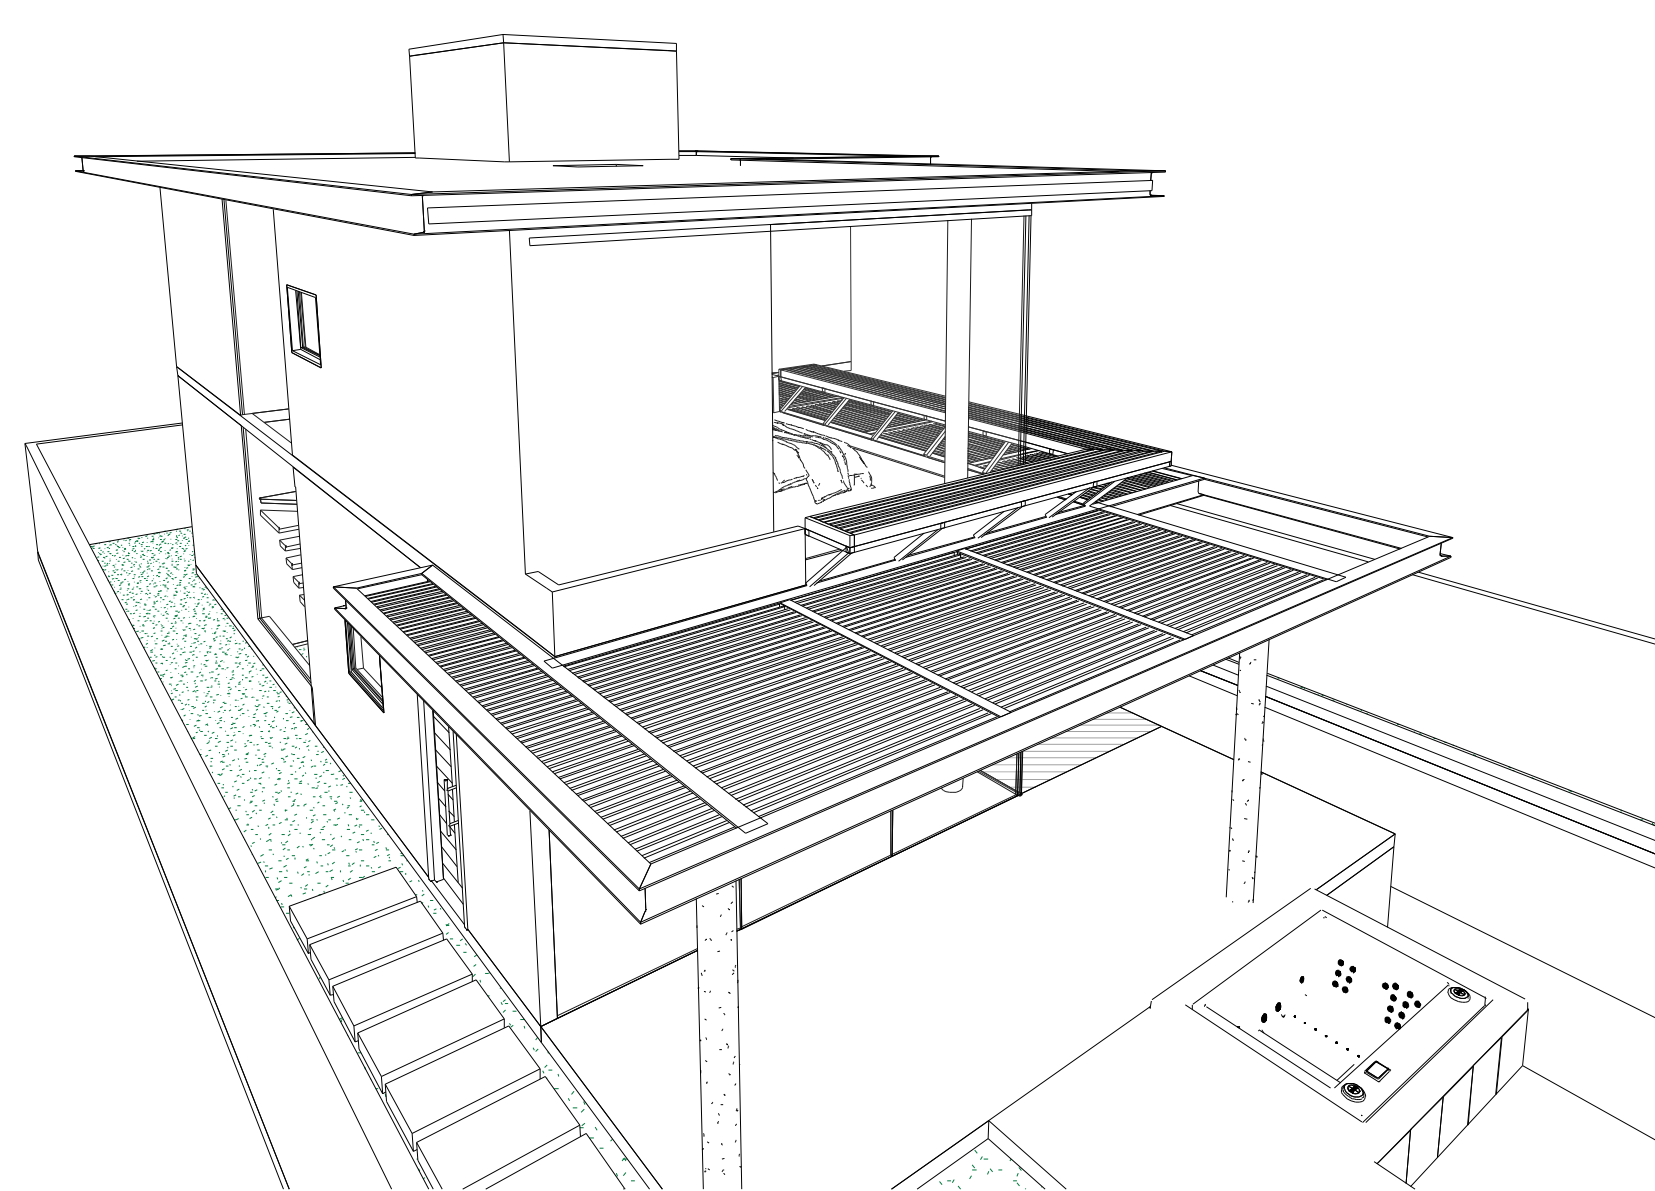

7 PERSPECTIVA 03

TABELA DE AMBIENTES		
AMBIENTE	ÁREA	NÍVEL
GARAGEM	25,64 m²	IMPLANTACÃO E PAV.01
FOCO DE CHÃO	13,25 m²	IMPLANTACÃO E PAV.01
VARANDA COBERTA	24,37 m²	IMPLANTACÃO E PAV.01
LAVABO 01	2,15 m²	IMPLANTACÃO E PAV.01
SALA DE TV	28,54 m²	IMPLANTACÃO E PAV.01
SALA DE JANTAR	20,37 m²	IMPLANTACÃO E PAV.01
COZINHA	23,60 m²	IMPLANTACÃO E PAV.01
ÁREA DE SERVIÇO	4,18 m²	IMPLANTACÃO E PAV.01
LAVABO 02	1,98 m²	IMPLANTACÃO E PAV.01
ÁREA GOURMET	35,45 m²	IMPLANTACÃO E PAV.01
DECK DE MADEIRA	18,00 m²	IMPLANTACÃO E PAV.01
PISCINA	47,86 m²	IMPLANTACÃO E PAV.01
SUITE MASTER	27,86 m²	IMPLANTACÃO E PAV.02
W.C. SUITE MASTER	3,85 m²	IMPLANTACÃO E PAV.02
HALL	5,95 m²	IMPLANTACÃO E PAV.02
SUITE 02	13,25 m²	IMPLANTACÃO E PAV.02
W.C. SUITE 02	3,60 m²	IMPLANTACÃO E PAV.02
SUITE 01	18,27 m²	IMPLANTACÃO E PAV.02
W.C. SUITE 01	3,60 m²	IMPLANTACÃO E PAV.02
Grand total: 19	301,02 m²	

QUADRO DE ESQUADRIAS - PORTAS				
TIPO	QUANTIDADE	LARGURA	ALTURA	DESCRIÇÃO
P1	2	0,60	2,10	ABRIR / 03 FOLHA
P2	3	0,70	2,10	ABRIR / 03 FOLHA
P3	1	0,80	2,10	ABRIR / 03 FOLHA
P4	3	0,70	2,10	DE CORRER - 01 FOLHA
P5	1	0,80	2,10	DE CORRER - 01 FOLHA
P6	1	1,20	1,20	LUXEIRA
Grand total: 11				

QUADRO DE ESQUADRIAS - JANELAS				
TIPO	QUANTIDADE	LARGURA	ALTURA	DESCRIÇÃO
J1	1	0,80	0,80	MAXIMAR
J2	4	1,20	0,80	MAXIMAR
J3	2	2,00	1,00	DE CORRER - 02 FOLHAS
Grand total: 7				

PROJETO:	TÉCNICO
PROPRIETÁRIO:	DOUGLAS ALBERTO BRAGA
LOCAL:	GUACÁ - SP
ASSUNTO:	CORTES
Arquiteto:	PAULO GVOZDEN
CONTATO:	12- 99192 3445
ESCALA	1 : 50
DATA	2022
FOLHA	A102