
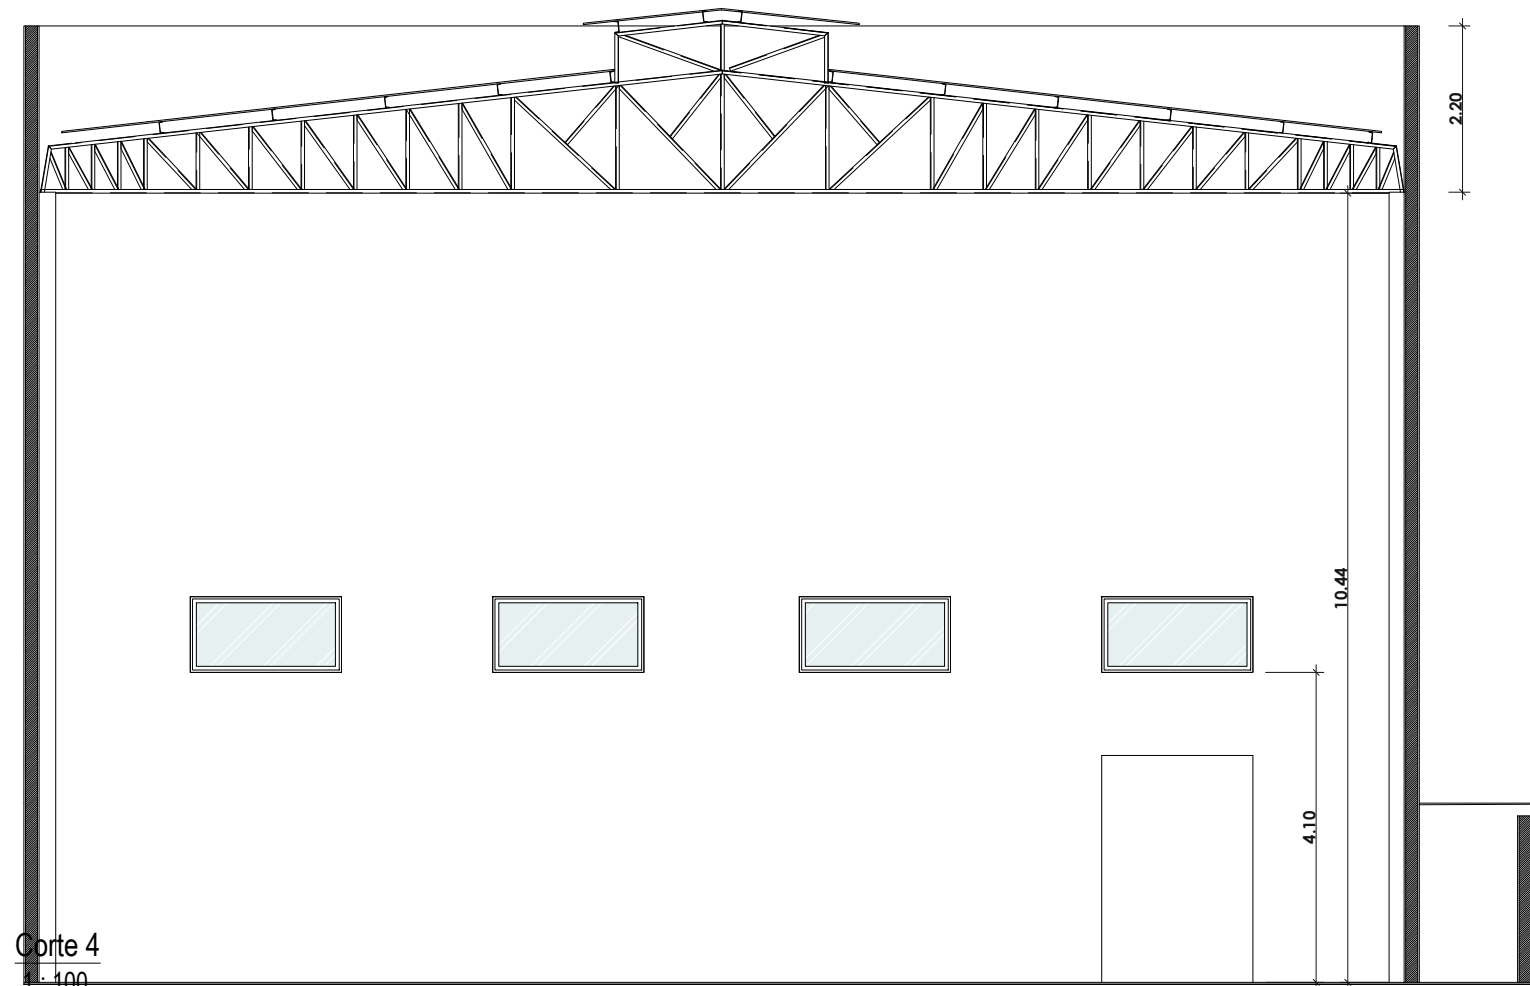


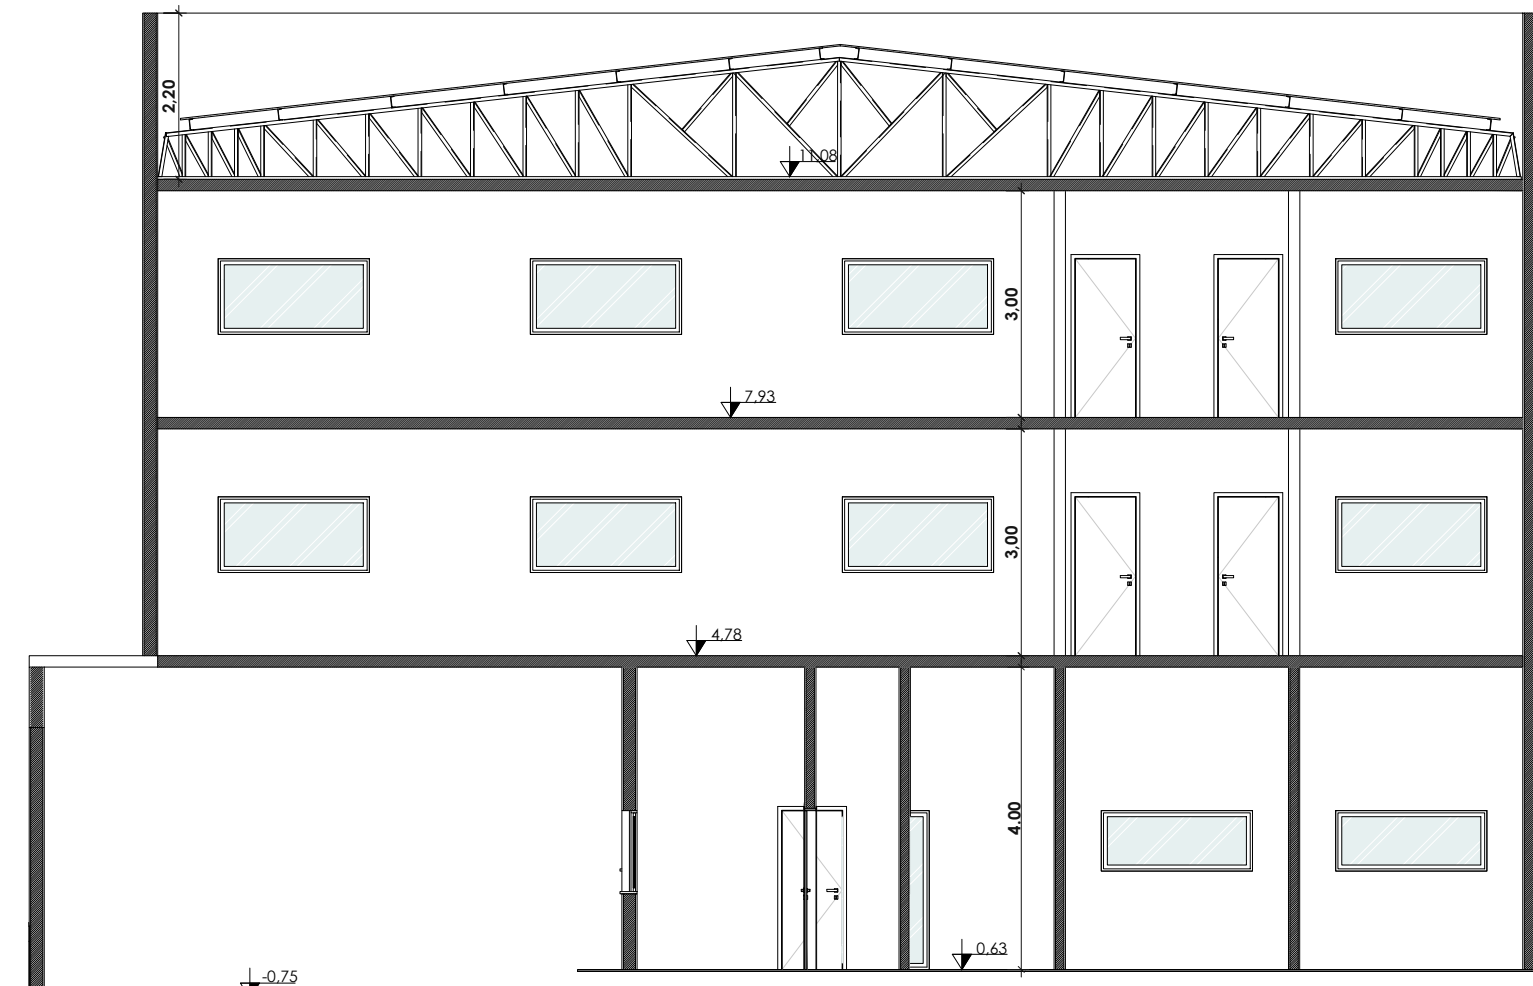

LEGENDA

- A CONSTRUIR
- PAV. TÉRREO
- MEZANINO 01
- MEZANINO 02

TABELA DE JANELAS						
Cód.	Quant.	Pelosi	Largura	Altura	Área	Descrição
J2	6	1,30 m	0,80 m	0,80 m	0,64 m²	Janela de vidro maxilar
J30	1	1,00 m	1,80 m	1,10 m	1,98 m²	Janela de vidro fixo
J38	12	1,10 m	2,00 m	1,00 m	2,00 m²	Janela de vidro maxilar
J39	2	1,30 m	2,00 m	0,80 m	1,60 m²	Janela de vidro maxilar
J40	4	4,10 m	2,00 m	1,00 m	2,00 m²	Janela de vidro maxilar

TABELA DE PORTAS					
Cód.	Quant.	Largura do Vão	Largura da Porta	Altura	Descrição
P1	11	0,86 m	0,80 m	2,10 m	Porta de Madeira com uma folha de abrir
P01	2	0,96 m	0,90 m	2,10 m	Porta de Madeira com uma folha de abrir
P7	1	1,80 m	1,74 m	2,84 m	Porta de Alumínio e Vidro com uma folha de correr
P8	1	5,00 m	5,00 m	3,30 m	Porta de Alumínio de enlomar
P9	1	2,00 m	2,00 m	3,00 m	Porta de Alumínio de enlomar

DECLARO QUE:

- PARA OS DEVIDOS FINS DE DIREITO, INCLUSIVE NA ESFERA PENAL, QUE O PROJETO FOI ELABORADO COM TOTAL OBSERVÂNCIA À LEGISLAÇÃO EM VIGOR VIGENTE, EM ESPECIAL DECRETOS, LEIS COMPLEMENTARES E LEIS MUNICIPAIS QUE DISPOEM RESPEITO AO USO E OCUPAÇÃO DO SOLO, CÓDIGO DE OBRAS DO MUNICÍPIO, NORMAS DE EDIFICAÇÕES E DEMAS CORRELATAS, TAMBÉM OBSERVANDO A NBR 9070 LEI ESTADUAL 10065/01 E DECRETO 12240/11.
- A CONSTRUÇÃO, MANUTENÇÃO E CONSERVAÇÃO DO PASSEIO PÚBLICO (CALÇADA) ATENDE À LEI MUNICIPAL Nº 2759/13.
- QUALQUER ALTERAÇÃO NO PROJETO SERÁ IMEDIATAMENTE COMUNICADA À PMH.
- DECLARO SER DE RESPONSABILIDADE DO PROPRIETÁRIO E DO RESPONSÁVEL TÉCNICO ATENDER ÀS NORMAS DE ACESSIBILIDADE PARA PORTADORES DE DEFICIÊNCIA OU COM MOBILIDADE REDUZIDA CONFORME LEGISLAÇÃO VIGENTE.

OBS: A PREFEITURA PODERÁ SOLICITAR INFORMAÇÕES ADICIONAIS QUE JULGAR NECESSÁRIAS AO AUTOR DO PROJETO OU AO PROPRIETÁRIO DA OBRA. ESTE PROJETO FOI ELABORADO COM BASE NAS MEDIDAS DO TERRENO CONSTANTES NA MATRÍCULA EXPEDIDA PELO CARTÓRIO DE REGISTRO DE IMÓVEIS.

PROJETO COMPLETO

F. ÚNICA

OBRA: CONSTRUÇÃO INDUSTRIAL

PROP.:

ENDEREÇO: Nº

LOTE: QUADRA:

LOTEAMENTO:

MUNICÍPIO DE INSCRIÇÃO IMOBILIÁRIA:

ESCALAS: INDICADAS

SITUAÇÃO SEM ESCALA

PROPRIETÁRIO(S):

CPF:

PROCURADOR(A):

CPF:

QUADRO DE ÁREAS

VIDE PROJETO INTERNO

RESPONSÁVEL TÉCNICO E AUTOR DO PROJETO

CAU: RPT PROJETO, RPT EXECUÇÃO:

ANOTAÇÕES PMH: